
Загальний план інженерних мереж

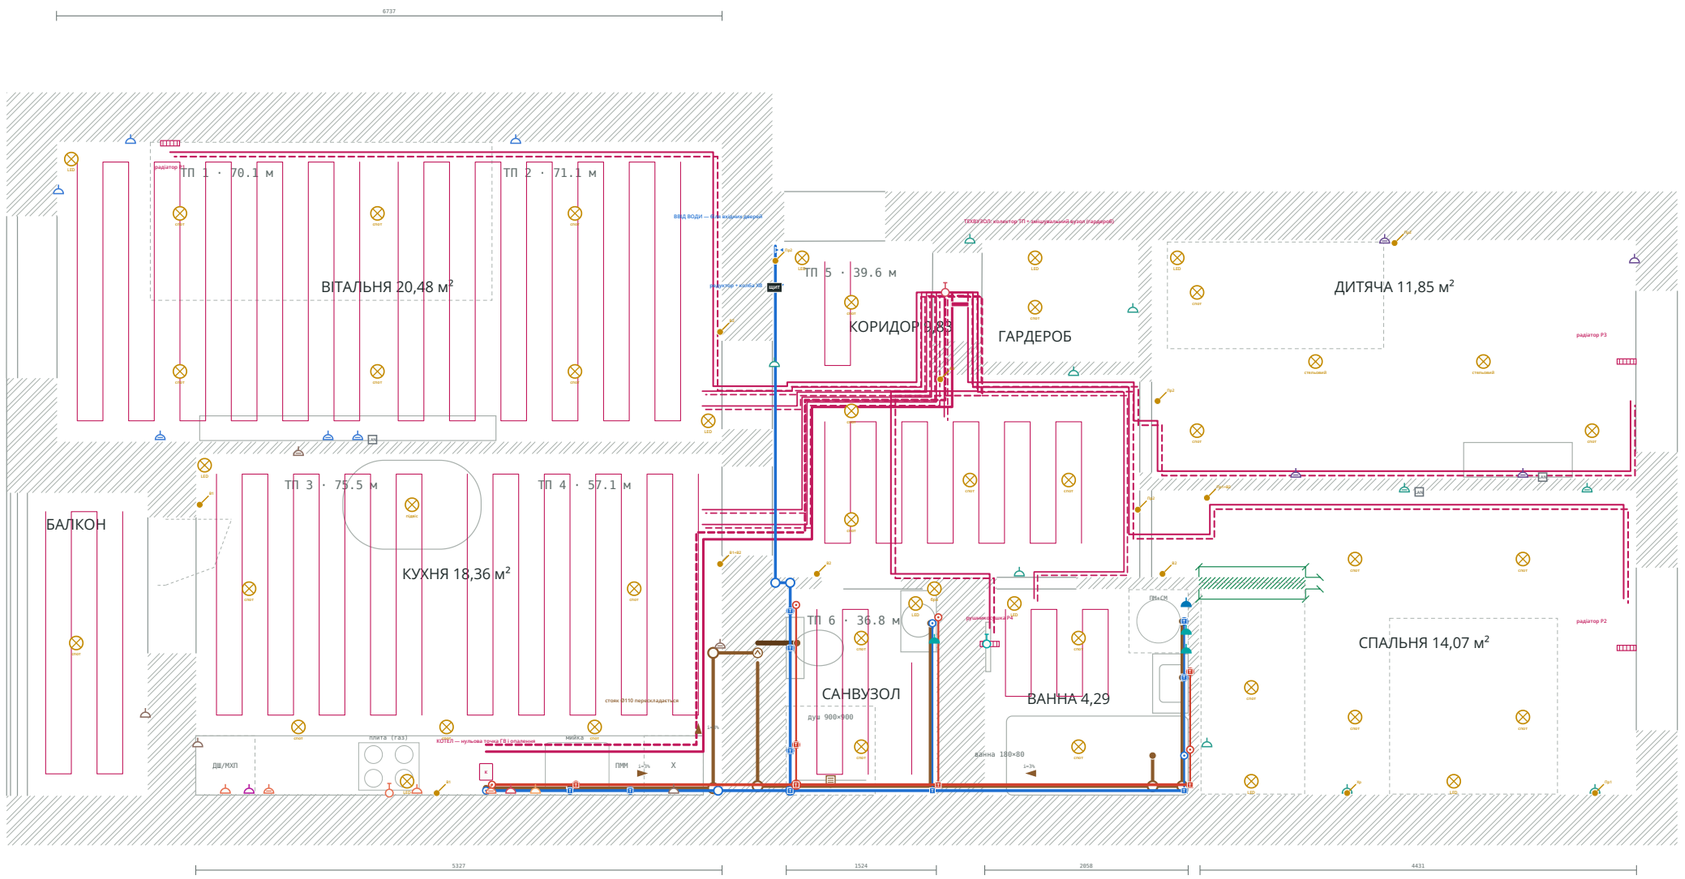

УМОВНІ ПОЗНАЧЕННЯ


- Холодна вода (товста — магістраль, тонка — відгалуження)
- Гаряча вода / опалення подача
- Трійник (Т)
- Коліно 90° на повороті
- Вивід води (настінне коліно)
- Кран кульовий
- Перехрещення (обвід)
- Тепла підлога: контур PEX-A 16×2,0 RED (схема петлі, крок 150/100)
- Опалення: подача / зворотка (магістраль Ø20, підвідні Ø16)
- Колектор теплої підлоги в шафі
- Радіатор
- Котел газовий двоконтурний
- Каналізація Ø50 / Ø32
- Каналізація Ø110
- Вивід каналізації
- Розетка (заливка — IP44, риска — 2-а)
- Вивід кабелю під прилад
- Світильник
- Вимикач

Розміри в мм. Н — висота від чистої підлоги. Траси орієнтовні, уточнюються під час монтажу.

ВИННИК РОМАН
САНТЕХНІКА · ОПАЛЕННЯ

Об’єкт	Квартира, Львів · 87,7 м² · Ekoplastik + Ostendorf
Аркуш	Загальний план інженерних мереж
Стадія	Підбір матеріалів за дизайн-проєктом
Розробив	**Винник Роман**, монтаж сантехніки та опалення, м. Львів
Дата	06.11.2026
Аркуш	1 з 14

Опалення: котел, технічний вузол, тепла підлога, радіатори

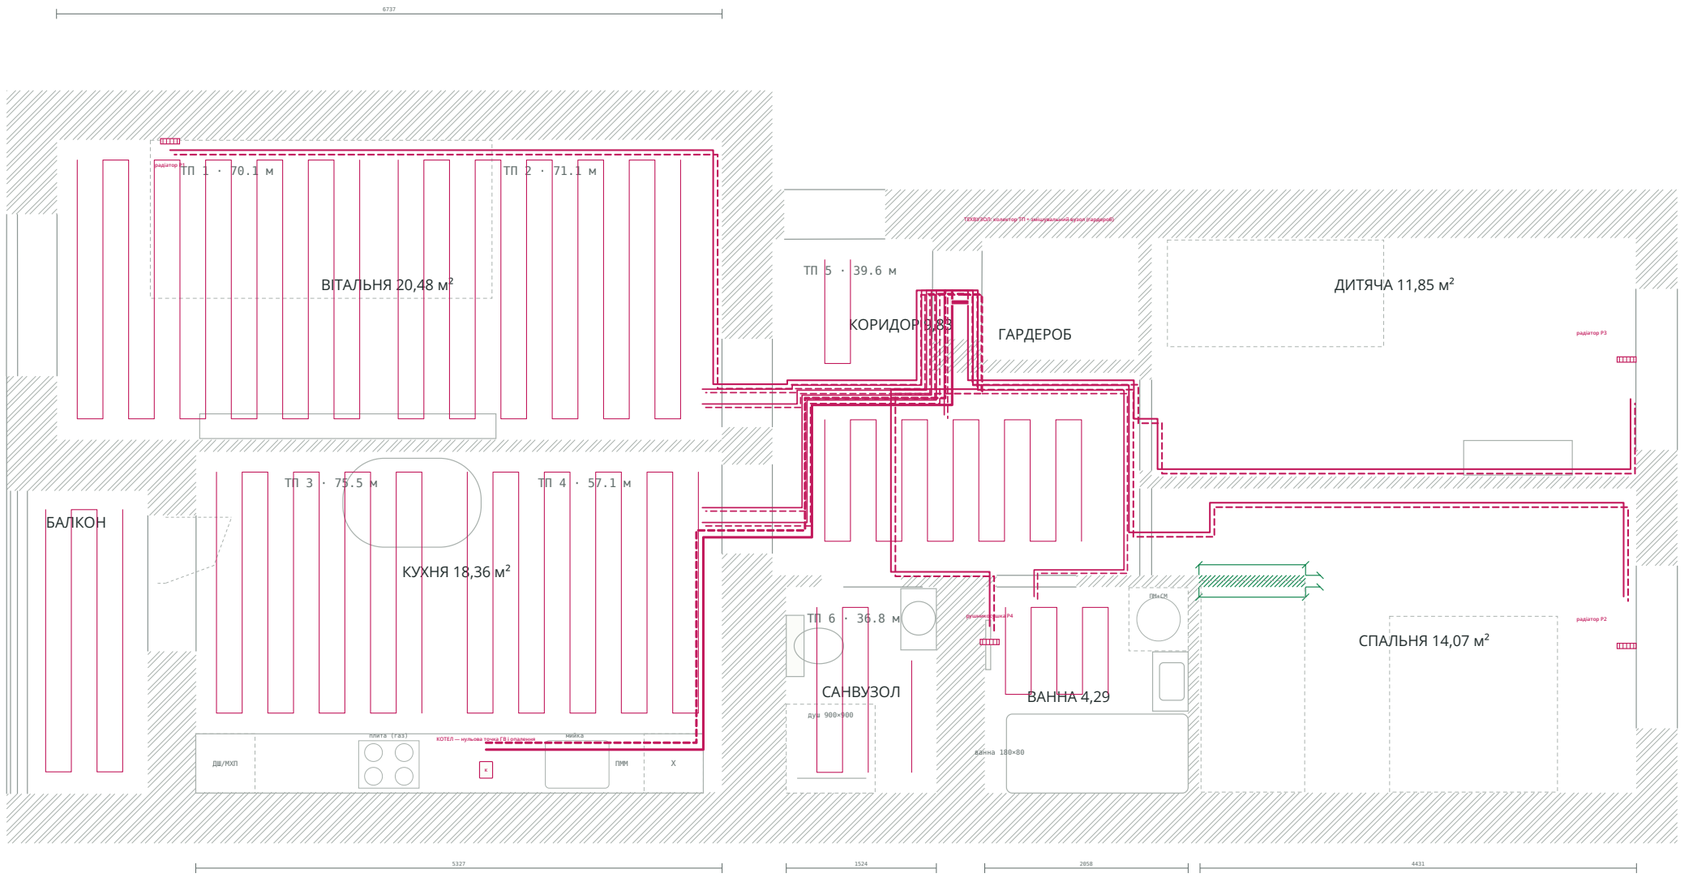

УМОВНІ ПОЗНАЧЕННЯ

- Тепла підлога: контур PEX-A 16×2,0 RED (схема петлі, крок 150/100)
- Колектор теплої підлоги в шафі
- Котел газовий двоконтурний
- Опалення: подача / зворотка (магістраль Ø20, підвідні Ø16)
- Радіатор

МАТЕРІАЛИ НА АРКУШІ


Опалення (тепла підлога)	
Котел BIASI 24 кВт 2-конт.	1
Змішувальний вузол SUR03 + насос	1
Контурів ТП (крок 150)	6
PEX-A 16×2,0 RED RAFTEC	350.2 м → 400 м
Радіатори (IDEALE ZETA 1, IDMAR 22 — 2) + рушникосушка водяна	4
Труба до радіаторів 16×2,2	115 м
Магістраль Ø20	35 м

Розміри в мм. Н — висота від чистої підлоги. Траси орієнтовні, уточнюються під час монтажу.

ВИННИК РОМАН
САНТЕХНІКА · ОПАЛЕННЯ

Об’єкт	Квартира, Львів · 87,7 м² · Ekoplastik + Ostendorf
Аркуш	Опалення: котел, технічний вузол, тепла підлога, радіатори
Стадія	Підбір матеріалів за дизайн-проєктом
Розробив	**Винник Роман**, монтаж сантехніки та опалення, м. Львів
Дата	06.11.2026
Аркуш	2 з 14

Водопостачання: холодна і гаряча вода

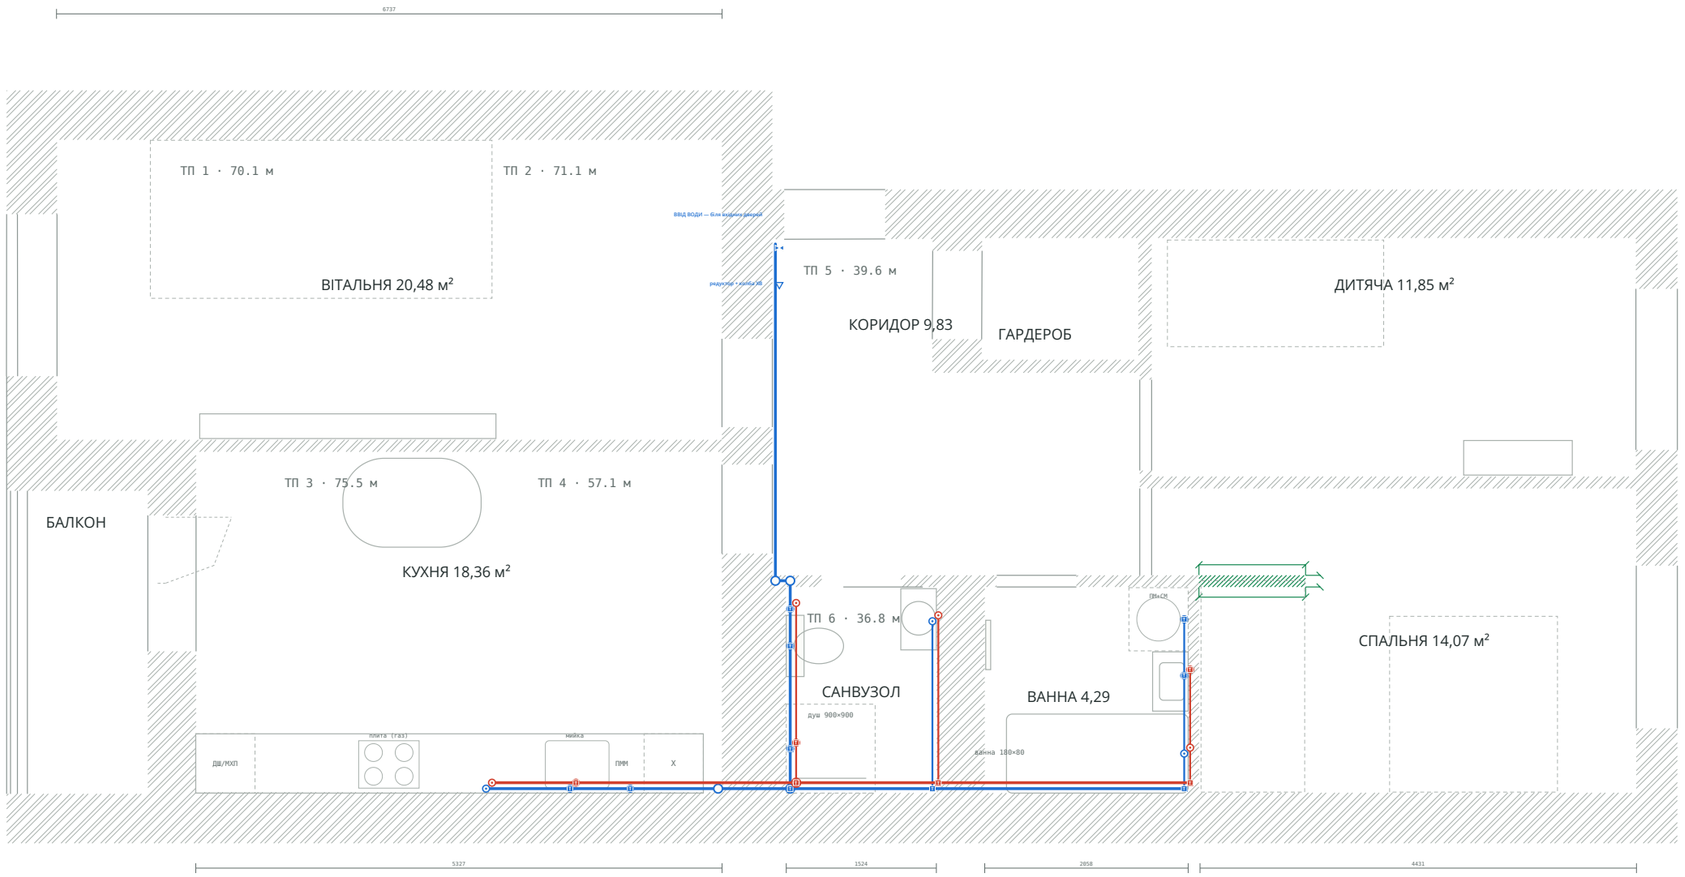

УМОВНІ ПОЗНАЧЕННЯ

- Холодна вода (товста — магістраль, тонка — відгалуження)
- Гаряча вода / опалення подача
- Трійник (Т)
- Коліно 90° на повороті
- Вивід води (настінне коліно)
- Кран кульовий
- Перехрещення (обвід)


МАТЕРІАЛИ НА АРКУШІ

Холодна вода	
PPR PN20 Ø25 Ekoplastik	32 м
PPR PN20 Ø20 Ekoplastik	24 м
Виводів ХВ	10
Гаряча вода	
PPR Fiber Basalt Ø25	20 м
PPR Fiber Basalt Ø20	20 м
Виводів ГВ (від котла)	7

Розміри в мм. Н — висота від чистої підлоги. Траси орієнтовні, уточнюються під час монтажу.

ВИННИК РОМАН
САНТЕХНІКА · ОПАЛЕННЯ

Об’єкт	Квартира, Львів · 87,7 м² · Ekoplastik + Ostendorf
Аркуш	Водопостачання: холодна і гаряча вода
Стадія	Підбір матеріалів за дизайн-проєктом
Розробив	**Винник Роман**, монтаж сантехніки та опалення, м. Львів
Дата	06.11.2026
Аркуш	3 з 14

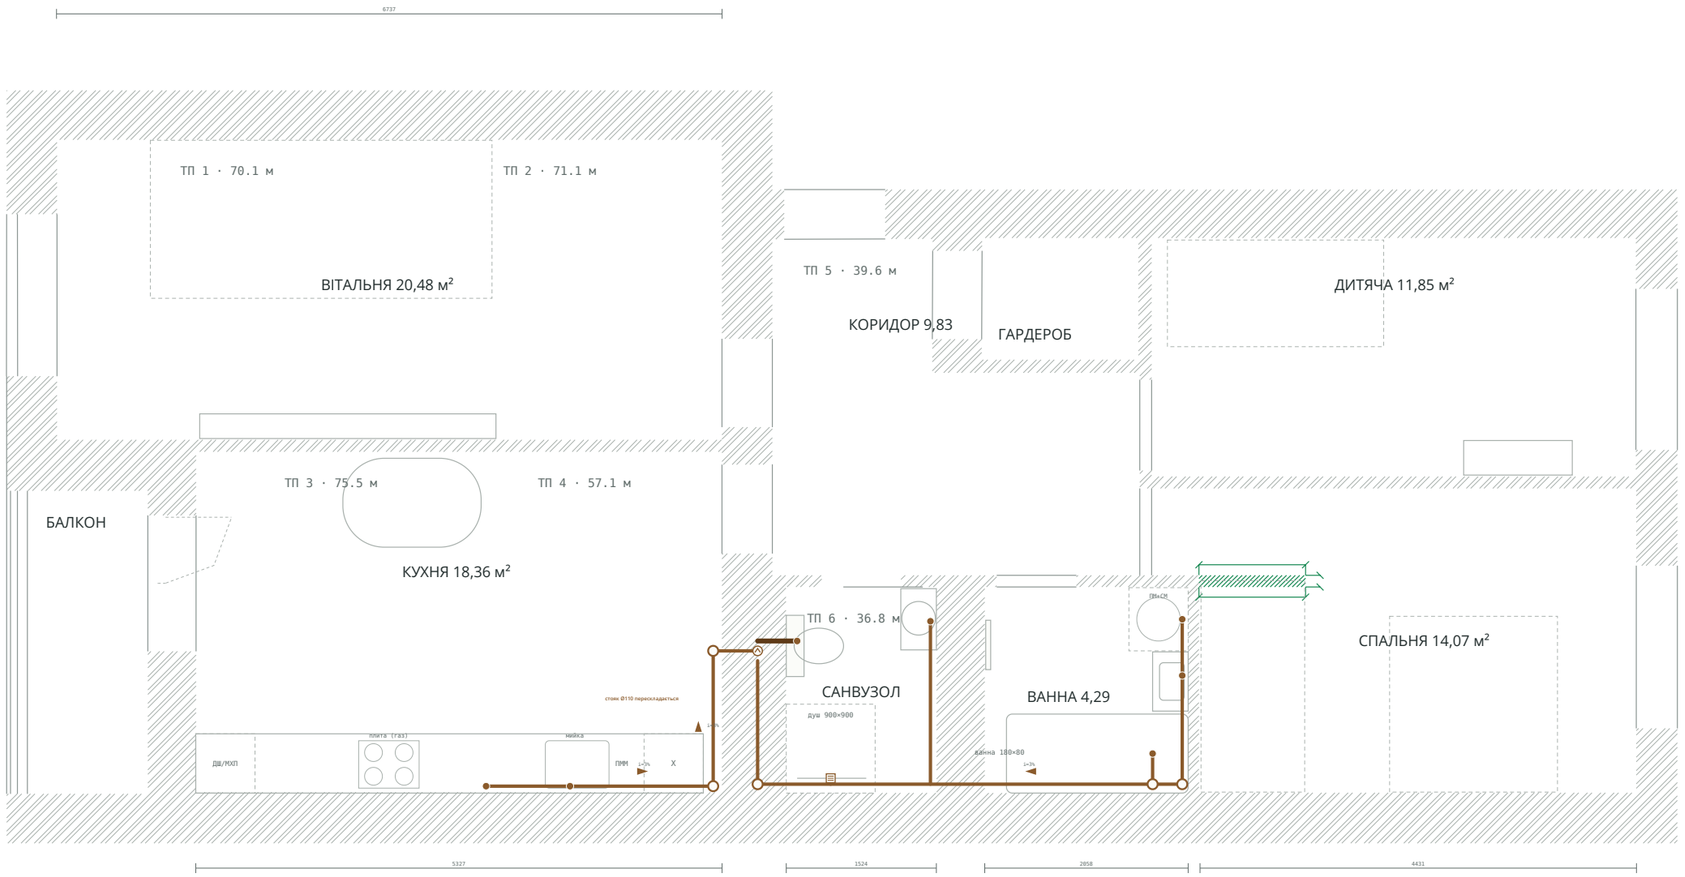

УМОВНІ ПОЗНАЧЕННЯ


- Каналізація Ø50 / Ø32
- Каналізація Ø110
- Вивід каналізації

МАТЕРІАЛИ НА АРКУШІ

Каналізація	
Ø50 OSTENDORF під стінами	19.2 м
Ø110 OSTENDORF (унітаз + стояк)	3.2 м
Трап ASG 700 Black	1

Розміри в мм. Н — висота від чистої підлоги. Траси орієнтовні, уточнюються під час монтажу.

ВИННИК РОМАН · САНТЕХНІКА · ОПАЛЕННЯ	
Об’єкт	Квартира, Львів · 87,7 м² · Ekoplastik + Ostendorf
Аркуш	Каналізація
Стадія	Підбір матеріалів за дизайн-проєктом
Розробив	**Винник Роман**, монтаж сантехніки та опалення, м. Львів
Дата	06.11.2026
Аркуш	4 з 14

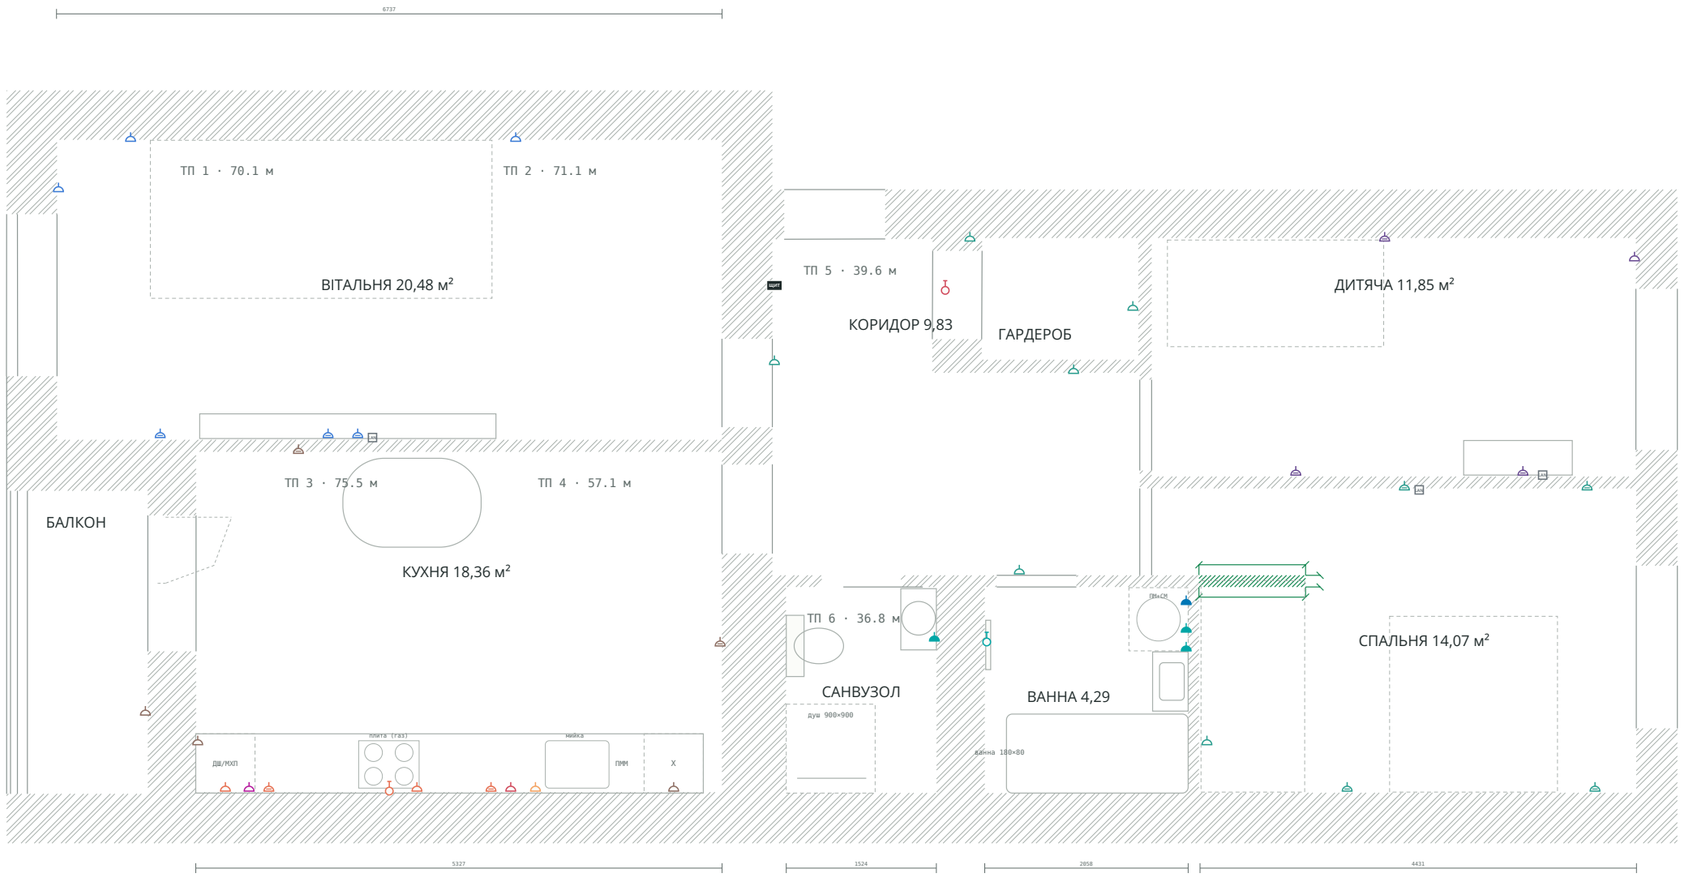

УМОВНІ ПОЗНАЧЕННЯ

- Розетка (заливка — IP44, риска — 2-а)
- Вивід кабелю під прилад

МАТЕРІАЛИ НА АРКУШІ

Розетки і виводи

Розеток 1-х	18
Розеток 2-х	14
IP44	4
Виводів	3
RJ45	3

ГРУПИ ЩИТА


Світло: коридор, гардероб, вітальня, кухня, балкон	C10 · 3x1,5 87.8 м
Світло: спальня, дитяча, санвузол, ванна	C10 · 3x1,5 79.4 м
Розетки вітальня	C16 · 3x2,5 32 м
Розетки коридор, гардероб, спальня	C16 · 3x2,5 49.3 м
Розетки дитяча	диф C16 30мА · 3x2,5 26.7 м
Кухня: стільниця, мікрохвильова, витяжка, підпал плити	диф C16 30мА · 3x2,5 21 м
Духова шафа	диф C16 30мА · 3x2,5 15.6 м
Посудомийна машина	диф C16 30мА · 3x2,5 12.4 м
Холодильник, ТВ кухні, обідня зона, балкон	C16 · 3x2,5 31.8 м
Пральна машина	диф C16 30мА · 3x2,5 11.4 м
Ванна і санвузол: розетки IP44, сушильна машина, рушникосушка	диф C16 30мА · 3x2,5 17.5 м
Котел газовий + насос змішувального вузла ТП	диф C16 30мА · 3x2,5 16.6 м
Інтернет: роутер → RJ45	— · FTP 32.9 м

Розміри в мм. Н — висота від чистої підлоги. Траси орієнтовні, уточнюються під час монтажу.

ВИННИК РОМАН
САНТЕХНІКА · ОПАЛЕННЯ

Об'єкт	Квартира, Львів · 87,7 м² · Ekoplastik + Ostendorf
Аркуш	Електрика: розетки, виводи, щит
Стадія	Підбір матеріалів за дизайн-проєктом
Розробив	**Винник Роман**, монтаж сантехніки та опалення, м. Львів
Дата	06.11.2026
Аркуш	5 з 14

Електрика: кабелі по групах щита

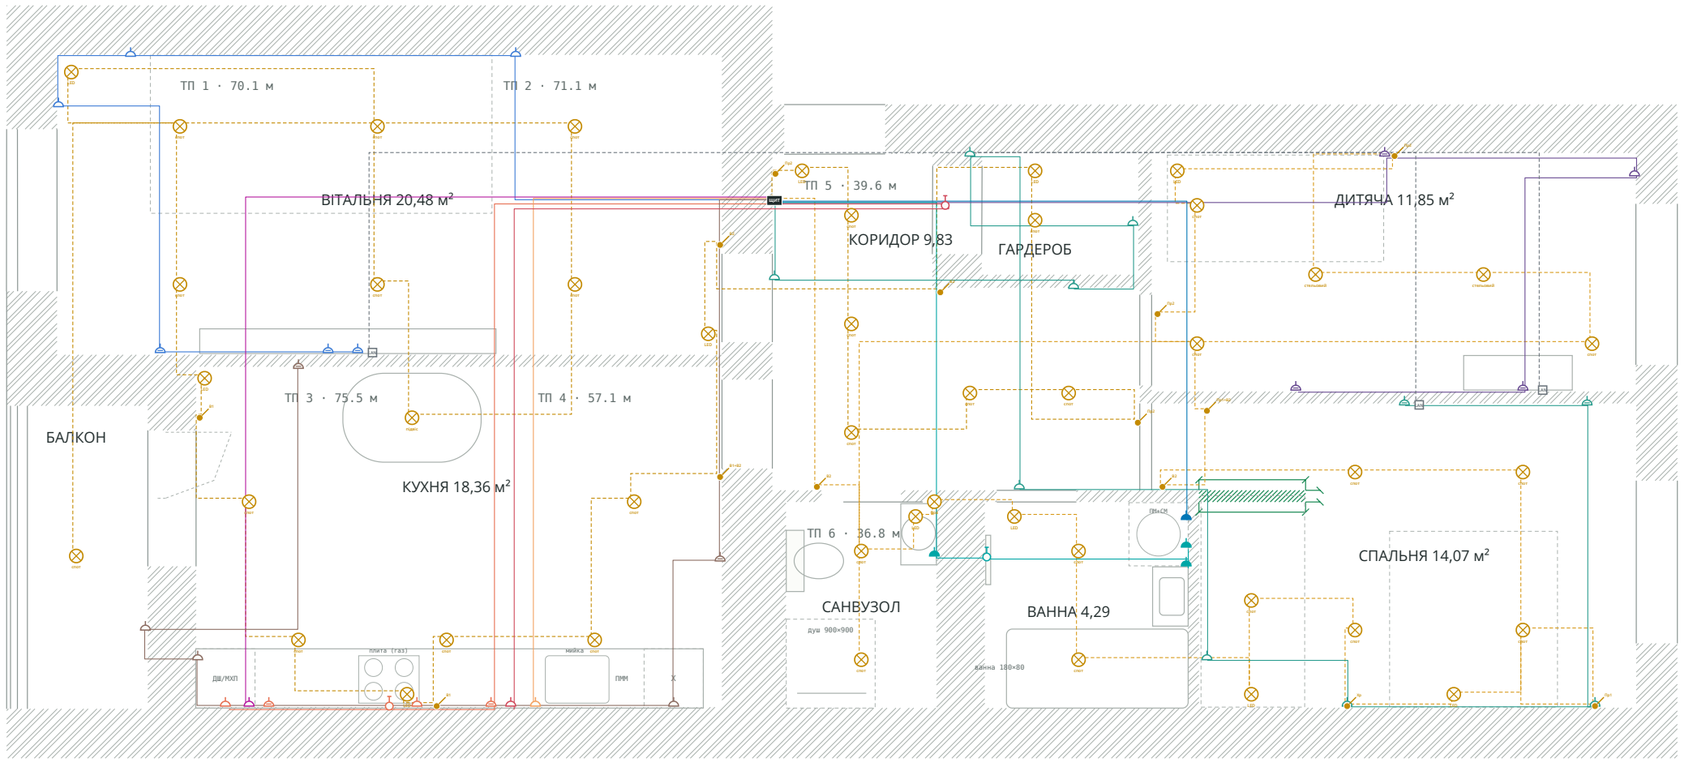

УМОВНІ ПОЗНАЧЕННЯ

- Кабель групи: суцільна — 3×2,5/3×4, штрих — 3×1,5/FTP
- Розетка (заливка — IP44, риска — 2-а)
- Вивід кабелю під прилад
- Світильник
- Вимикач

МАТЕРІАЛИ НА АРКУШІ

Розетки і виводи	
Розеток 1-х	18
Розеток 2-х	14
IP44	4
Виводів	3
RJ45	3
Кабелі	
3x1,5 RAFTEC	210 м
3x2,5 RAFTEC	220 м
FTP 5e	35 м
Освітлення	
Точок світла	45
Постів вимикачів	14

ГРУПИ ЩИТА

Світло: коридор, гардероб, вітальня, кухня, балкон	C10 · 3x1,5 87.8 м
Світло: спальня, дитяча, санвузол, ванна	C10 · 3x1,5 79.4 м
Розетки вітальня	C16 · 3x2,5 32 м
Розетки коридор, гардероб, спальня	C16 · 3x2,5 49.3 м
Розетки дитяча	диф C16 30мА · 3x2,5 26.7 м
Кухня: стільниця, мікрохвильова, витяжка, підпал плити	диф C16 30мА · 3x2,5 21 м
Духова шафа	диф C16 30мА · 3x2,5 15.6 м
Посудомийна машина	диф C16 30мА · 3x2,5 12.4 м
Холодильник, ТВ кухні, обідня зона, балкон	C16 · 3x2,5 31.8 м
Пральна машина	диф C16 30мА · 3x2,5 11.4 м
Ванна і санвузол: розетки IP44, сушильна машина, рушникосушка	диф C16 30мА · 3x2,5 17.5 м
Котел газовий + насос змішувального вузла ТП	диф C16 30мА · 3x2,5 16.6 м
Інтернет: роутер → RJ45	— · FTP 32.9 м

Розміри в мм. Н — висота від чистої підлоги. Траси орієнтовні, уточнюються під час монтажу.

ВИННИК РОМАН
САНТЕХНІКА · ОПАЛЕННЯ

Об’єкт	Квартира, Львів · 87,7 м² · Ekoplastik + Ostendorf
Аркуш	Електрика: кабелі по групах щита
Стадія	Підбір матеріалів за дизайн-проєктом
Розробив	**Винник Роман**, монтаж сантехніки та опалення, м. Львів
Дата	06.11.2026
Аркуш	6 з 14



УМОВНІ ПОЗНАЧЕННЯ

Світильник

Вимикач


МАТЕРІАЛИ НА АРКУШІ

Освітлення	
Точок світла	45
Постів вимикачів	14

Розміри в мм. Н — висота від чистої підлоги. Траси орієнтовні, уточнюються під час монтажу.

ВИННИК РОМАН
САНТЕХНІКА · ОПАЛЕННЯ

Об’єкт	Квартира, Львів · 87,7 м² · Ekoplastik + Ostendorf
Аркуш	Освітлення і вимикачі
Стадія	Підбір матеріалів за дизайн-проєктом
Розробив	**Винник Роман**, монтаж сантехніки та опалення, м. Львів
Дата	06.11.2026
Аркуш	7 з 14

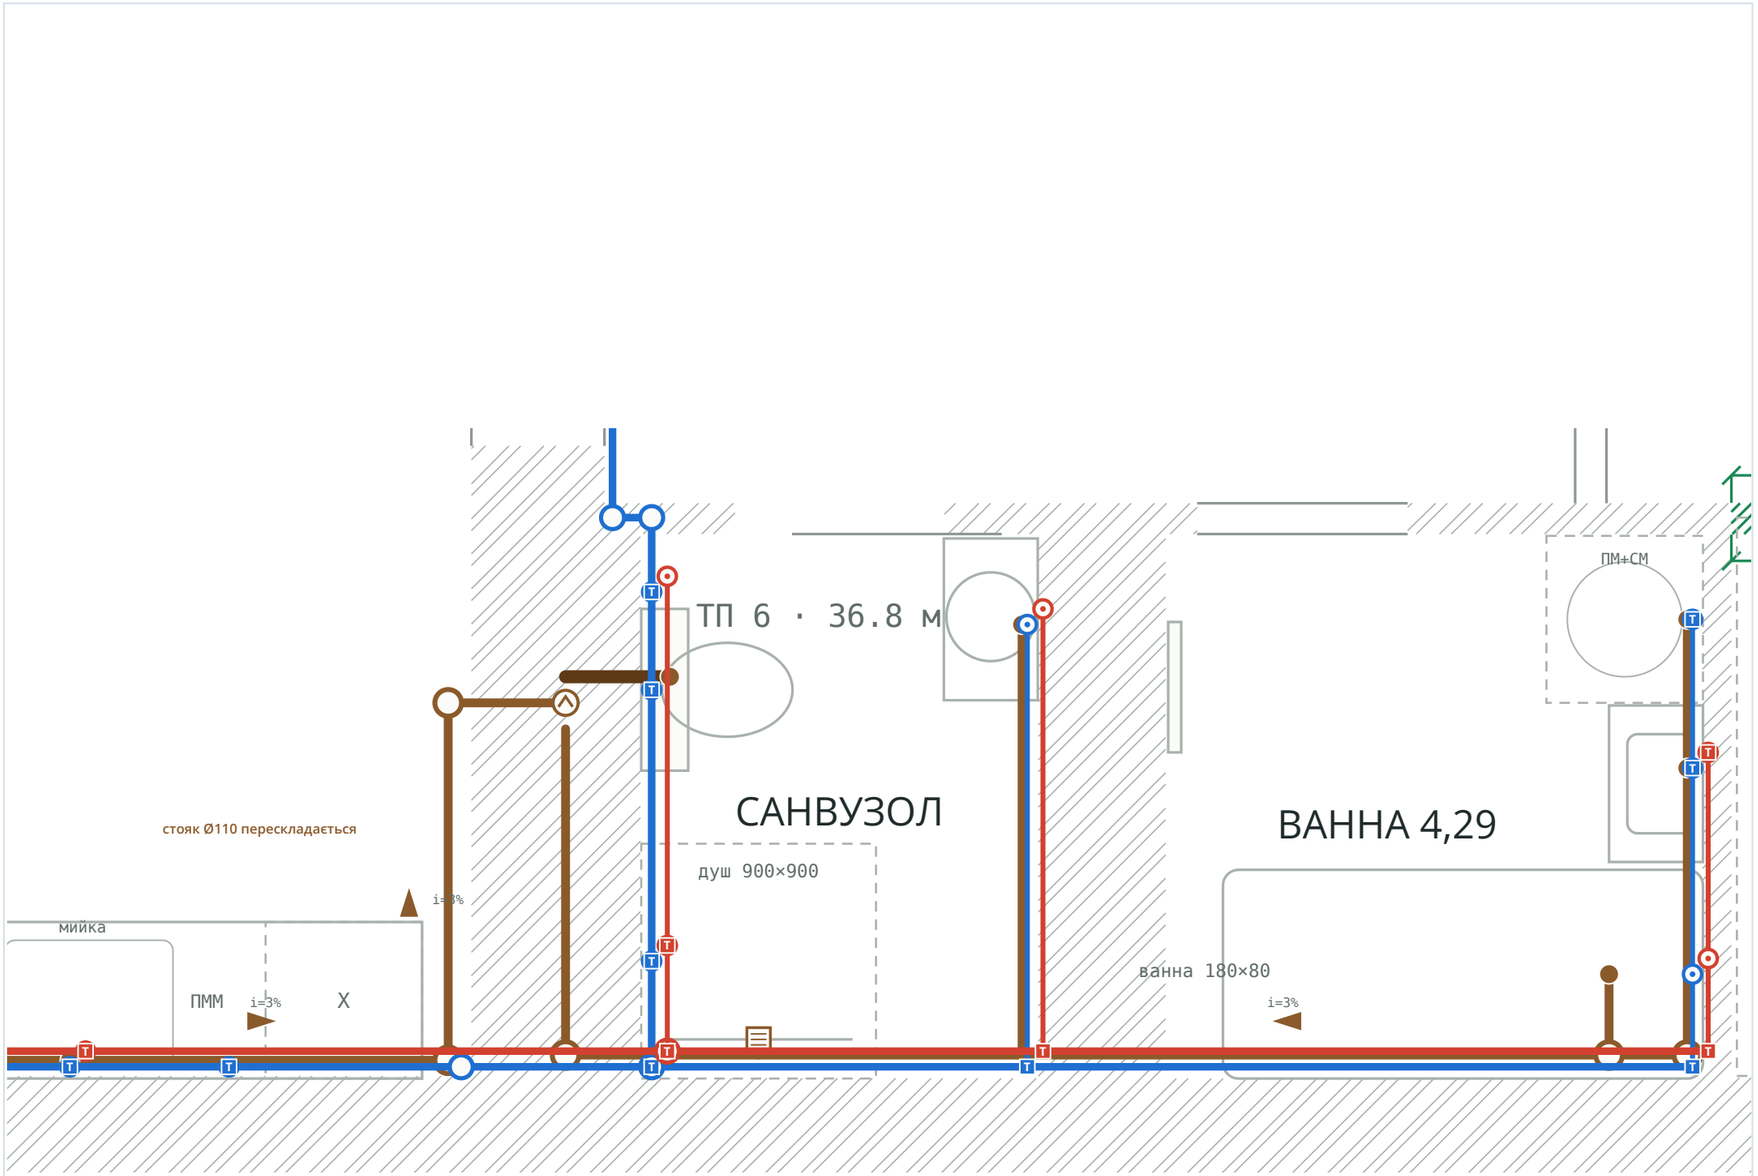

УМОВНІ ПОЗНАЧЕННЯ

- Холодна вода (товста — магістраль, тонка — відгалуження)
- Гаряча вода / опалення подача
- Трійник (Т)
- Коліно 90° на повороті
- Вивід води (настінне коліно)
- Кран кульовий
- Перехрещення (обвід)
- Каналізація Ø50 / Ø32
- Каналізація Ø110
- Вивід каналізації

МАТЕРІАЛИ НА АРКУШІ

Холодна вода	
PPR PN20 Ø25 Ekoplastik	32 м
PPR PN20 Ø20 Ekoplastik	24 м
Виводів ХВ	10
Гаряча вода	
PPR Fiber Basalt Ø25	20 м
PPR Fiber Basalt Ø20	20 м
Виводів ГВ (від котла)	7
Каналізація	
Ø50 OSTENDORF під стінами	19.2 м
Ø110 OSTENDORF (унітаз + стояк)	3.2 м
Трап ASG 700 Black	1

Розміри в мм. Н — висота від чистої підлоги. Траси орієнтовні, уточнюються під час монтажу.

ВИННИК РОМАН
САНТЕХНІКА · ОПАЛЕННЯ

Об'єкт	Квартира, Львів · 87,7 м² · Ekoplastik + Ostendorf
Аркуш	Мокра зона збільшено: вода і каналізація
Стадія	Підбір матеріалів за дизайн-проєктом
Розробив	**Винник Роман**, монтаж сантехніки та опалення, м. Львів
Дата	06.11.2026
Аркуш	8 з 14

№	Код	Артикул	Найменування	К-сть	Од.
Чорнова сантехніка (опалення, водопостачання і каналізація)					
1	00000098445	GRDV01	Кран кульовий В3, DN15, 1/2'', PN64, GRDV01, CW617N, метелик, RAFTEC GOLD {35/140}	1	шт
2	00000072197	FKU-01	Фільтр груб. очистки, DN15, 1/2", під пломбу, BLACK, RAFTEC {40/160}	1	шт
3	00000074162		Лічильник хол. води DN15 1/2", L110 E-C 2,5, ECOSTAR (зі штуцерами) {20}	1	шт
4	00000055736	KL01	Зворотний клапан для води, ВВ, DN15, 1/2", KL01, RAFTEC {75/300}	1	шт
5	00000089999	RCFR01-C	Редуктор з самопромив. фільтр. DN15, 1/2", для хол. води, з маном., латунь, RCFR01-C, RAFTEC {5/10}	1	шт
6	00000095614		Фільтр-колба SENIOR PLUS 3P, 1/2", ZA111T111, MFO SX TS, ATLAS FILTRI	1	шт
7	00000046408	CPV251020ECO	Картридж зі спіненого поліпропілену, 2,5"x10", 20 мкм, Ecosoft {48}	2	шт
8	00000098451	GRDS01	Кран кульовий з амер. В3, DN15, 1/2'', PN64, GRDS01, метелик, RAFTEC GOLD {20/80}	3	шт
9	00000051901	N01	Ніпель, латунь, 33, DN15, 1/2", нікель, RAFTEC {10/120/480}	4	шт
10	00000042976	SZE02520XX	Муфта PPR МР3, ф 25x1/2", PP-RCT, Ekoplastik {10/100}	1	шт
11	00000000966	STR025P20X	Труба PPR PN20 ф 25x4,2 мм, PP-RCT, Ekoplastik {4/60}	32	м
12	00000043026	STR020P20X	Труба PPR PN20 ф 20x3,4 мм, PP-RCT, Ekoplastik {4/100}	24	м
13	00000043030	STRFB025TRCT	Труба PPR Fiber Basalt ф 25x3,5 мм, PN20, PP-RCT, Ekoplastik {4/60}	20	м
14	00000021920	STRFB020TRCT	Труба PPR Fiber Basalt ф 20x2,8 мм, PN20, PP-RCT, Ekoplastik {4/100}	20	м
15	00000043179	STKR02520X	Трійник редукційний PPR, ф 25x20x25, PP-RCT, Ekoplastik {20/120}	12	шт
16	00000000928	STK025RCTX	Трійник рівний PPR, ф 25, PP-RCT, Ekoplastik {20/100}	2	шт
17	00000043009	STK020RCTX	Трійник рівний PPR, ф 20, PP-RCT, Ekoplastik {20/180}	5	шт
18	00000007750	SRE12520RCT	Муфта перехідна PPR ЗВ, ф 25x20, PP-RCT, Ekoplastik {20/360}	4	шт
19	00000042938	SKO02090RCT	Коліно PPR 90°, ф 20, PP-RCT, Ekoplastik {20/260}	70	шт
20	00000000564	SKO02590RCT	Коліно PPR 90°, ф 25, PP-RCT, Ekoplastik {20/140}	10	шт
21	00000000555	SKO02045XX	Коліно PPR 45° ф 20, PP-RCT, Ekoplastik {20/300}	28	шт
22	00000000556	SKO02545RCT	Коліно PPR 45° ф 25, PP-RCT, Ekoplastik {20/160}	6	шт
23	00000000650	SNA020RCTX	Муфта PPR ф 20, PP-RCT, Ekoplastik {20/360}	11	шт
24	00000000651	SNA025RCTX	Муфта PPR ф 25, PP-RCT, Ekoplastik {20/220}	13	шт
25	00000043204	SNKD02020X	Планка для змішувача PPR, ф 20x1/2", PP-RCT, Ekoplastik {10/50}	3	шт
26	00000043083	SNK020XRCT	Коліно настінне PPR РВ, ф 20x1/2", PP-RCT, Ekoplastik {10/120}	10	шт
27	00000042974	SZE02020XX	Муфта PPR МР3, ф 20x1/2", PP-RCT, Ekoplastik {10/140}	1	шт

Кількості з розрахунку за дизайн-проєктом. Довжини вводу води, випуску каналізації та ввідного кабелю уточнюються на об'єкті. Ціни — в окремому рахунку.

ВИННИК РОМАН
САНТЕХНІКА · ОПАЛЕННЯ

Об'єкт	Квартира, Львів · 87,7 м² · Ekoplastik + Ostendorf
Аркуш	Специфікація матеріалів
Стадія	Підбір матеріалів за дизайн-проєктом
Розробив	**Винник Роман**, монтаж сантехніки та опалення, м. Львів
Дата	06.11.2026
Аркуш	9 з 14

Специфікація матеріалів (продовження)

№	Код	Артикул	Найменування	К-сть	Од.
28	00000043224	ZAGDXXXXXX	Заглушка різьбова довга PPR P3, 1/2", PP-RCT, Ekoplastik {50/150}	17	шт
29	00000069934		Утеплювач ламін. для труб ф 22х6 мм, синій, PLM {2/300}	24	м
30	00000069931		Утеплювач ламін. для труб ф 22х6 мм, червоний, PLM {2/300}	55	м
31	00000069935		Утеплювач ламін. для труб ф 28х6 мм, синій, PLM {2/230}	32	м
32	00000069932		Утеплювач ламін. для труб ф 28х6 мм, червоний, PLM {2/230}	20	м
33	00000085209	38811KF0	Інсталяція для підвісного унітазу,3в1,1,13 м висота установки,клав.Even Black,Solido 38811KF0 Grohe	1	шт
34	00000014853	172060	Труба вн. канал. ф 50 х 1,8 мм, L = 2,0 м, сіра, HT Safe, OSTENDORF {10}	5	шт
35	00000014852	172040	Труба вн. канал. ф 50 х 1,8 мм, L = 1,0 м, сіра, HT Safe, OSTENDORF {10}	5	шт
36	00000014851	172020	Труба вн. канал. ф 50 х 1,8 мм, L = 0,5 м, сіра, HT Safe, OSTENDORF {20}	6	шт
37	00000014850	172010	Труба вн. канал. ф 50 х 1,8 мм, L = 0,25 м, сіра, HT Safe, OSTENDORF {20}	6	шт
38	00000014887	172140	Коліно вн. канал. ф 50 х 87,5°, сіре, HT Safe, OSTENDORF {18}	7	шт
39	00000014886	172120	Коліно вн. канал. ф 50 х 45°, сіре, HT Safe, OSTENDORF {20}	24	шт
40	00000061171	172200	Трійник вн. канал. ф 50 х 50 х 45°, сірий, HT Safe, OSTENDORF {20}	5	шт
41	00000017999	175040	Труба вн. канал. ф110 х 2,7 мм, L = 1,0 м, сіра, HT Safe, OSTENDORF {4}	1	шт
42	00000018003	175020	Труба вн. канал. ф110 х 2,7 мм, L = 0,5 м, сіра, HT Safe, OSTENDORF {10}	2	шт
43	00000018002	175120	Коліно вн. канал. ф110 х 45°, сіре, HT Safe, OSTENDORF {16/20}	2	шт
44	00000015859	175400	Трійник вн. канал. ф110 х 110 х 87,5°, сірий, HT Safe, OSTENDORF {8}	1	шт
45	00000014935	175420	Трійник вн. канал. ф110 х 50 х 87,5°, сірий, HT Safe, OSTENDORF {20}	2	шт
46	00000014978	175600	Ревізія вн. канал. ф110, сіра, HT Safe, OSTENDORF {20}	1	шт
47	00000014842	175800	Патрубок компенсаційний вн. канал. ф110. сірий. HT Safe. OSTENDORF {20}	1	шт
48	00000070558	175820	Перехід з чавуна на пластик вн. канал. ф110, сірий, HT Safe, OSTENDORF {20}	2	шт
49	00000018766	172720	Редукція ексентрична довга вн. канал. ф 50 х 32, сіра, HT Safe, OSTENDORF {20}	3	шт
50	00000014839	172620	Заглушка вн. канал. ф 50, сіра, HT Safe, OSTENDORF {20}	7	шт
51	00000014838	175620	Заглушка вн. канал. ф110, сіра, HT Safe, OSTENDORF {20}	1	шт
52	00000012413		Хомут, DN 40, 1 1/2", ф 47-53, стальний, з кріпленням, гайка M8*100, KVADO {120}	18	шт
53	00000110904	6556877	Хомут для труб 4" 108-112 мм, M10x100 мм, ASG	4	шт
54	00000125085	HL400	Вбудований сифон DN40/50 для пральних або посудомийних машин	1	шт
55	00000111587	6557137	Трап для душу, 360 °, сухий затвір, 700 мм, 04 P black, ASG, (п/з)	1	шт

Кількості з розрахунку за дизайн-проєктом. Довжини вводу води, випуску каналізації та ввідного кабелю уточнюються на об’єкті. Ціни — в окремому рахунку.

ВИННИК РОМАН
САНТЕХНІКА · ОПАЛЕННЯ

Об’єкт	Квартира, Львів · 87,7 м² · Ekoplastik + Ostendorf
Аркуш	Специфікація матеріалів (продовження)
Стадія	Підбір матеріалів за дизайн-проєктом
Розробив	**Винник Роман**, монтаж сантехніки та опалення, м. Львів
Дата	06.11.2026
Аркуш	10 з 14

Специфікація матеріалів (продовження)

№	Код	Артикул	Найменування	К-сть	Од.
56	00000040884	881810	Мастило технічне вн. канал. 250 мг., HT Safe, OSTENDORF {50}	1	шт
57	00000079872	M275V.2024 SM	Котел газовий конденсаційний 24 кВт, 2-конт, RINNOVA COND, BIASI {6}	1	шт
58	00000038603	71.MT7.00.08	Комплект коаксиальної димової труби конденсаційного котла, ф 60/100 мм, 71.MT7.00.08	1	шт
59	00000098452	GRDS02	Кран кульовий з амер. В3, DN20, 3/4'', PN50, GRDS02, метелик, RAFTEC GOLD {15/60}	2	шт
60	00000098620	RMGHB02	Фільтр магнітний кутовий з накид. гайкою ЗВ, DN20, 3/4". RMGHB02, метелик, RAFTEC BLACK {20}	1	шт
61	00000068436	RPXA20100-1	Труба (част) PEX-A, ф 20x2,8 мм, EVOH, SILVER, RAFTEC	35	м
62	00000058593	PWM2002	Коліно натяжне настінне, ф 20x3/4", PB, PUSH, RAFTEC {60/100/240}	2	шт
63	00000058576	PSN2002	Муфта натяжна, ф 20x3/4", P3, PUSH, RAFTEC {100/240/400}	2	шт
64	00000103797	GF0302	Футорка, латунь, ЗВ, DN25x20, 1"x3/4", RAFTEC GOLD {50/200}	2	шт
65	00000058599	PT201620	Трійник натяжний, ф 20x16x20, PUSH, RAFTEC {5/30/120}	8	шт
66	00000100219	RMPPB20	Фіксатор повороту труби, 90°, ф20 мм, сталь нерж., RAFTEC {200}	12	шт
67	00000103828	GZN02	Заглушка, латунь, P3, DN20, 3/4", під пломбу, RAFTEC GOLD {100/400}	2	шт
68	00000055875	SUR03	Змішувальний вузол 1", латунь, нікель, SUR03, RAFTEC {5}	1	шт
69	00000085522		Насос циркуляційний енергозберігаючий APE 25/40/130 мм PWM1 AUTO Termojet	1	шт
70	00000098616	RVMK03	Комплект кранів кульових з накид. гайкою ВВ, DN25, 1", RAFTEC (пара) {2/16}	1	шт
71	00000055867	RC03-06	Колектор 6-и контр., 1"x3/4", витратоміри, без єврокон., нерж., RAFTEC STEEL {6}	1	шт
72	00000055879	KKR03	Кінцевий елемент 1", латунь, нікель, RAFTEC {25/60}	2	шт
73	00000109073	6558049	Колекторна шафа №4, вріз., 795x575-665x110-175 мм, ASG	1	шт
74	00000102028		Радіатор дизайнерський IDEALE ZETA 12 12/1800/548 білий мат., універ. підключ.	1	шт
75	00000116159	22607	Кран дизайн з термоголовкою кутовий IDEALE 1/2" x 1/2" B3 білий мат. пара	1	шт
76	00000058591	PVV1601	Коліно натяжне настінне, ф 16x1/2", PB, PUSH, RAFTEC, LV {60/120/240}	4	шт
77	00000113267	V22500X100	Радіатор сталевий, тип 22, 500x1000, VK, нижне підключення, Eco Heat, IDMAR	1	шт
78	00000113265	V22500X080	Радіатор сталевий, тип 22, 500x 800, VK, нижне підключення, Eco Heat, IDMAR	1	шт
79	00000098646	DAHU11-W	Термокомплект нижнього підключення кутовий з термоголовкою, WHITE, RAFTEC {10/50}	2	шт
80	00000060396	EKRC-16-34-22	Євроконус 3/4" x ф 16x2,2 мм, хром, RAFTEC {100/120/400}	4	шт
81	00000068435	RPXA16100-1	Труба (част) PEX-A, ф 16x2,2 мм, EVOH, SILVER, RAFTEC	115	м
82	00000069930		Утеплювач ламін. для труб ф 18x6 мм, червоний, PLM {2/400}	115	м
83	00000100218	RMPPB16	Фіксатор повороту труби, 90°, ф16 мм, сталь нерж., RAFTEC {200}	34	шт

Кількості з розрахунку за дизайн-проєктом. Довжини вводу води, випуску каналізації та ввідного кабелю уточнюються на об'єкті. Ціни — в окремому рахунку.

ВИННИК РОМАН
САНТЕХНІКА · ОПАЛЕННЯ

Об'єкт	Квартира, Львів · 87,7 м² · Ekoplastik + Ostendorf
Аркуш	Специфікація матеріалів (продовження)
Стадія	Підбір матеріалів за дизайн-проєктом
Розробив	**Винник Роман**, монтаж сантехніки та опалення, м. Львів
Дата	06.11.2026
Аркуш	11 з 14

Специфікація матеріалів (продовження)

№	Код	Артикул	Найменування	К-сть	Од.
84	00000060395	EKRC-16-34-20	Євроконус 3/4" х ф 16х2,0 мм, хром, RAFTEC {100/120/400}	12	шт
85	00000057229	RPXA16200-S	Труба PEX-A, ф 16х2,0 мм, RED, EVOH, Spain, RAFTEC {200}	400	м
86	00000058502		Труба захисна, D20, гофрована, червона, AQUAPEX {50}, пог.м	18	м
87	00000109656	RFDTP50	Плівка з розміткою 105мкм, рулон 50м, Raftec	2	шт
88	00000048693		Демпферна стрічка шир.16,5 см, товщ.7 мм, довж. 50 м, EXTRA {50}	100	м
89	00000108659		Демпферна стрічка міжконтурна (хімзшита), пог.м	5	м
90	00000090902		Скоба гарпун, 42 мм, під такер, ф16-20, Standart {700/8 400}	1400	шт
91	00000058571	PG20	Гільза натяжна, ф 20, PUSH, RAFTEC {10/180/720}	20	шт
92	00000058570	PG16	Гільза натяжна, ф 16, PUSH, RAFTEC {300/800/1 200}	12	шт
93	00000018277	GD1MM	Вставка діелектрична д/газу 1/2", 33, Ecoflex {50}	1	шт
94	00000028460		Шланг газовий, ВВ, 1/2", 1,0м., білий, ПВХ, Алєксєєнко {20}	1	шт
95	00000115129		Однофазний стабілізатор напруги АНТС У 600 (1ф, 600Вт) Елекс	1	шт
96	00000031509	0.1005/1800014001	Добавка в бетон: BETOKAN 10 л {10}	1	шт
97	00000000775	PRE020XXXX	Опора PPR, ф 20, PP-RCT, Ekoplastik {50/500}	70	шт
98	00000042960	PRE025XXXX	Опора PPR, ф 25, PP-RCT, Ekoplastik {50/500}	80	шт
99	00000003044		Кліпса для металопластикової труби, 16х2, з застібкою {100/2 000}	150	шт
100	00000003045		Кліпса для металопластикової труби, 20х2, з застібкою {100/1 500}	50	шт
101	00000103963	ДМГ1 06401	Дюбель швидкого монтажу 6х40 гриб з шурупом (уп.100шт) Ziplex (ДМГ1 06401) {100}	4	уп
102	00000103971	ДМП1 08801	Дюбель швидкого монтажу 8х80 потай з шурупом (уп.100 шт) Ziplex (ДМП1 08801)	1	уп
103	00000094514	61007210	Універсальний нейлоновий дюбель М10х50мм WUP, Walraven	4	шт
Чистова сантехніка					
1	00000105049	39554000	Унітаз настінного монтажу з сидінням, Euro Ceramic Grohe	1	шт
2	00000102407	UA111197243	Гігієнічний комплект,чорний, Tempesta-F, Essence Grohe	1	шт
3	00000059550	K114-007	Раковина меблева, біла, квадратна, на стільницю CREA 35 см, Cersanit	1	шт
4	00000083589	LIG081NO	Змішувач для раковини, з високим виливом, чорний мат, Light Paffoni	2	шт
5	00000098700	1024642430	Донний клапан для умивальника, матовий чорний, Grohe	2	шт
6	00000103071		Сифон пляшковий для умивальника низький 1 1/4*32 без зливу НС 2 McAlpine	2	шт
7	00000122093	703	Кран кульовий кутовий ARCO 1/2″ x 1/2″ A-80 NOV06 приборний	6	шт

Кількості з розрахунку за дизайн-проєктом. Довжини вводу води, випуску каналізації та ввідного кабелю уточнюються на об'єкті. Ціни — в окремому рахунку.

ВИННИК РОМАН
САНТЕХНІКА · ОПАЛЕННЯ

Об'єкт	Квартира, Львів · 87,7 м² · Ekoplastik + Ostendorf
Аркуш	Специфікація матеріалів (продовження)
Стадія	Підбір матеріалів за дизайн-проєктом
Розробив	**Винник Роман**, монтаж сантехніки та опалення, м. Львів
Дата	06.11.2026
Аркуш	12 з 14

Специфікація матеріалів (продовження)

№	Код	Артикул	Найменування	К-сть	Од.
8	00000122081	1053362430+35604000	Душова система прих.монтажу на 2 виходи, Tempesta 250, Cubeo чорний мат + SmartBox, Grohe	2	шт
9	00000098270		Душова кабіна, AS Ethos 90 ALL BLACKS, 90*90, прозрачные дверцы стекло 5 мм, профиль черный	1	шт
10	00000115933		Дзеркало Standart Solito C 700мм, передня підсвітка, чорна рамка + вимикач сенсор, Wells	1	шт
11	00000110689	K114-005	Раковина накладна на стільницю, прямокутна, CREA 50, Cersanit	1	шт
12	00000057682	S301-227	Ванна акрилова, 180x80, прям., з ніжками CREA Cersanit	1	шт
13	00000118122	44917	Сифон для ванни Click-Clack чорний матовий Cersanit	1	шт
14	00000092153		Шторка на ванну, 700 R, h 2040, прозора, профіль RAL9005(black) mat, WERDER Liberta	1	шт
15	00000093094		Рушникосушарка водяна Dexter П15 500x1000 Deffi нержавіюча сталь (Чорний, Нижнє пі	1	шт
16	00000093417		Кран кутовий під ТЕН G1/2" комплект 2шт. чорний мат	1	шт
17	00000102819		ТЕН OnlyHeat Onyx Black Pro 0,6 кВт (прихований монтаж)	1	шт
18	00000091090		Кран кульовий кутовий ARCO 1/2"x 3/4" DEF728P AntiLime	2	шт
19	00000113167		Дзеркало VARIO (NESSO) 400x900, Liberta	1	шт
20	00000093421	VS 50 10 03	Мийка кухонна гранітна, прямокутна з крилом, avena, 645x495x200, VS501003, Stone, VENTA	1	шт
21	00000080199	PM 40 SF 20 03	Сифон для мийки 1 1/2"*40, гофротр. 40x40/50 з литим вип, відвед. до прал.машин, PLM {40}	1	шт
22	00000090706	BK813BB	Змішувач для кухні, чорний, гнучкий вилив, з підк осмосу, sus 304, карт 35 мм, BK813BB VENTA LW {10}	1	шт
23	00000112883		Тримач паперу закритий "ROLL black", Liberta	1	шт
24	00000112884		Щітка для унітазу "ROLL black", Liberta	1	шт
25	00000112885		Гачок для рушників "ROLL black", Liberta	2	шт
26	00000105994		Полиця Loft 500мм, чорна, Liberta	2	шт
Чорнова електрика (щит, кабель, розетки, вимикачі, коробки)					
1	00000117071	EZ9EUB312	Щит пласт. ЩРВ-П-36 мод вбудов.уст. IP30 з білими дверима Easy9 EU Schneider (EZ9EUB312)	1	шт
2	00000104546	EZ9F34240	Автоматичний вимикач, 2 полюси, 40A, C, 4,5kA, Easy9(EZ9), чорний перемикач, Schneider (EZ9F34240) {	1	шт
3	00000110306		Реле напруги ZUBR D40T (40A, підключ. низ, 3 Din, контроль/демонстація напруги, термозахист)	1	шт
4	00000114600	EZ9D34616	Диференційний автомат, 1P+N, 16A, EASY9 C, 30mA, AC, 4.5kA, чорний перемикач, Schneider (EZ9D34616)	7	шт
5	00000104533	EZ9F34116	Автоматичний вимикач, 1 полюс, 16A, C, 4,5kA, Easy9(EZ9),чорний перемикач, Schneider (EZ9F34116) 1	3	шт
6	00000104532	EZ9F34110	Автоматичний вимикач, 1 полюс, 10A, C, 4,5kA, Easy9(EZ9), чорний перемикач, Schneider (EZ9F34110) 1	2	шт
7	00000123995	RNYIFY-J-315	Кабель ВВГнг-П 3x1,5, RAFTEC (плоский, моножила, чорний) (100)	210	м
8	00000123996	RNYIFY-J-325	Кабель ВВГнг-П 3x2,5, RAFTEC (плоский, моножила, чорний) (100)	240	м

Кількості з розрахунку за дизайн-проєктом. Довжини вводу води, випуску каналізації та ввідного кабелю уточнюються на об’єкті. Ціни — в окремому рахунку.

ВИННИК РОМАН
САНТЕХНІКА · ОПАЛЕННЯ

Об’єкт	Квартира, Львів · 87,7 м² · Ekoplastik + Ostendorf
Аркуш	Специфікація матеріалів (продовження)
Стадія	Підбір матеріалів за дизайн-проєктом
Розробив	**Винник Роман**, монтаж сантехніки та опалення, м. Львів
Дата	06.11.2026
Аркуш	13 з 14

Специфікація матеріалів (продовження)

№	Код	Артикул	Найменування	К-сть	Од.
9	00000109661	7091000	Кабель FTP(F/UTP) cat.5e 4x2x24(0,51) AWG 100 МГц,33КМ (інтернет,екранований,сірий,внутрішній) {305}	35	м
10	00000110283	1416E_K50D	Гофротруба, ф16 мм,з протяжкою,негорюча,320N,ПВХ,світло-сіра,KOPOS MONOFLEX(50м) {50}	150	м
11	00000110284	1420_K50D	Гофротруба, ф20 мм,з протяжкою,негорюча,320N,ПВХ,світло-сіра,KOPOS MONOFLEX(50м) {50}	150	м
12	00000112332	SDD311221	Розетка 2-а з З/К внутр. зі шторками Білий "Sedna Design" Schneider (SDD311221)	14	шт
13	00000116415	SDD211024	Розетка 1-а З/К внутр. зі шторками та кришкою IP44 Білин "Sedna Design" Schneider (SDD211024)	4	шт
14	00000112098	SDD111022	Розетка 1-а З/К внутр. зі шторками Білий "Sedna Design" Schneider (SDD111022)	18	шт
15	00000123547	SDD111903	Розетка для виводу кабеля Білий Sedna Design (SDD111903)	3	шт
16	00000112327	SDD111451	Розетка 1-а комп. внутр. RJ45 кат. 5e UTP Білий "Sedna Design" Schneider (SDD111451)	3	шт
17	00000112096	SDD111101	Вимикач 1-кл. внутр. Білий "Sedna Design" Schneider (SDD111101)	3	шт
18	00000109506	SDD111105	Вимикач 2-кл. внутр. Білий "Sedna Design" Schneider (SDD111105)	6	шт
19	00000112093	SDD111106	Перемикач 1-кл. внутр. Білий "Sedna Design" Schneider (SDD111106)	2	шт
20	00000112330	SDD111108	Перемикач 2-кл Білий "Sedna Design" Schneider (SDD111108)	4	шт
21	00000109518	SDD311801	Рамка 1-о кратна Білий "Sedna Design" Schneider (SDD311801)	40	шт
22	00000112971	SDD111107	Перехресний вимикач внутр. "Sedna Design" Білий (SDD111107)	1	шт
23	00000109519	SDD311802	Рамка 2-х кратна Білий "Sedna Design" Schneider (SDD311802)	2	шт
24	00000104325		Коробка установча, глибока 65х60мм, д/бетону, набірна, з шурупами, UNIKA PLANK MB003, зелена {150}	72	шт
25	00000104338		Коробка розподільча, д/бетону, Ø70х40мм, з кришкою, UNIKA PLANK MB101, зелена {170}	38	шт
26	00000103922		Клема 3-конт д/розпод коробок, універсальна, 0,2-4 мм2, прозора, 221-413 WAGO (50)	150	шт
27	00000103927		Клема 5-конт д/розпод коробок, універсальна, 0,2-4 мм2, прозора, 221-415 WAGO(25)	40	шт
28	00000103981	ДХК 16001	Дюбель-хомут «Ялинка» для круглого кабелю ф16 мм, поліпропілен, білий Ziplex (уп.50 шт) (ДХК 16001)	6	уп
29	00000103982	ДХК 20001	Дюбель-хомут «Ялинка» для круглого кабелю ф20 мм, поліпропілен, білий Ziplex (уп.50 шт) (ДХК 20001)	6	уп
30	00000113742	502016	Стяжка кабельна (хомут) біла 4х200 (3,6х200мм) (100шт) TAKEL (502016) {100}	2	уп

Кількості з розрахунку за дизайн-проєктом. Довжини вводу води, випуску каналізації та ввідного кабелю уточнюються на об’єкті. Ціни — в окремому рахунку.

ВИННИК РОМАН
САНТЕХНІКА · ОПАЛЕННЯ

Об’єкт	Квартира, Львів · 87,7 м² · Ekoplastik + Ostendorf
Аркуш	Специфікація матеріалів (продовження)
Стадія	Підбір матеріалів за дизайн-проєктом
Розробив	**Винник Роман**, монтаж сантехніки та опалення, м. Львів
Дата	06.11.2026
Аркуш	14 з 14